




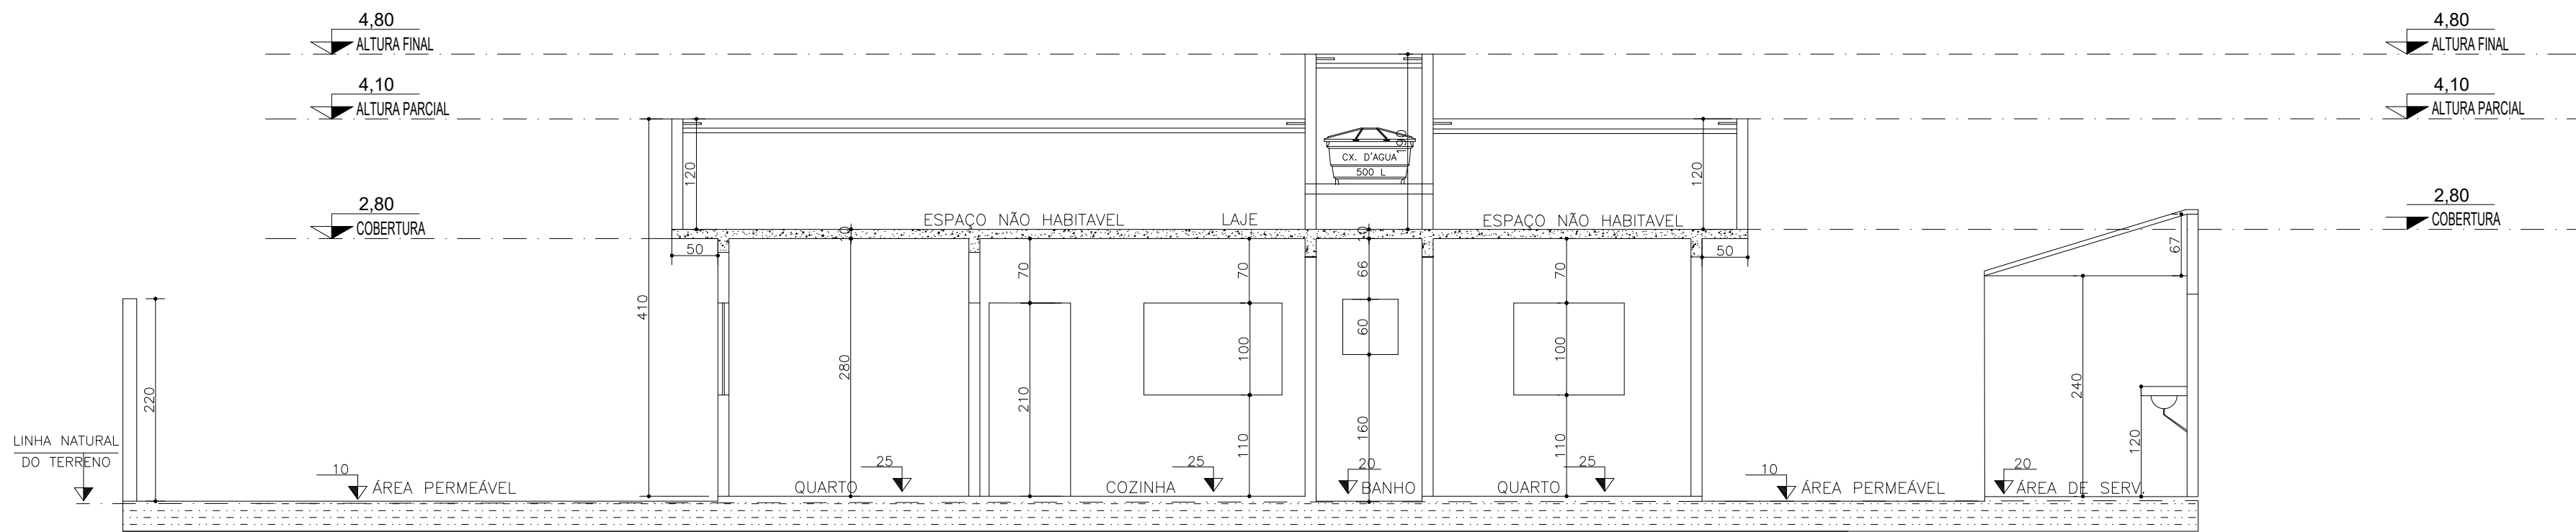

CORTE A A – 1:100

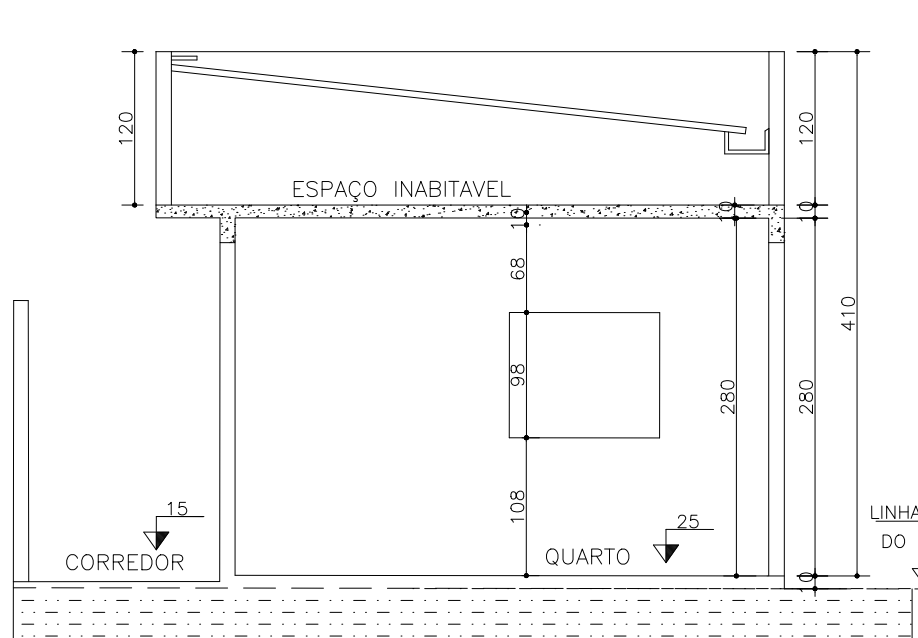

CORTE B B – 1:100

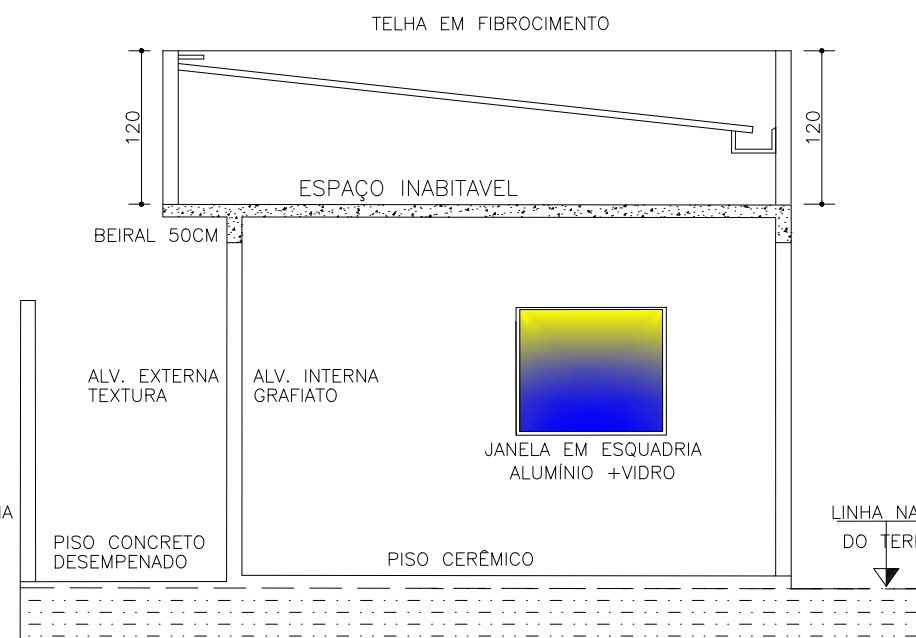


FACHADA – 1:100


QUADRO DE ABERTURAS		
	MEDIDAS	MATERIAIS
P1	90X210	VIDRO
P2	80X210	MADERA
P3	60X210	MADERA
P4	80X210	MADERA
J1	100X120	ALUMINIO; VIDRO
J2	150X100	ALUMINIO; VIDRO
J3	60X60	ALUMINIO; VIDRO
J4	135X100	ALUMINIO; VIDRO

Materiais – Revestimento	
Parede interna	Revestimento grafiato
Parede externa	Textura
Piso interno	Revestimento 60x60
Piso externo	Piso concreto desempenado


QUADRO DE ÁREAS – HABITAÇÃO UNIFAMILIAR					
UNIDADE	PAV. TERREO	TOTAL	ÍNDICE PAISAGISTICO	FRAÇÃO	VAGA
CASA 1	60,71m²	60,71m²	30,96m²Em cob.vegetal	138,00m²	01
TOTAL	60,71m²	60,71m²	30,96m²Em cob.vegetal	138,00m²	01

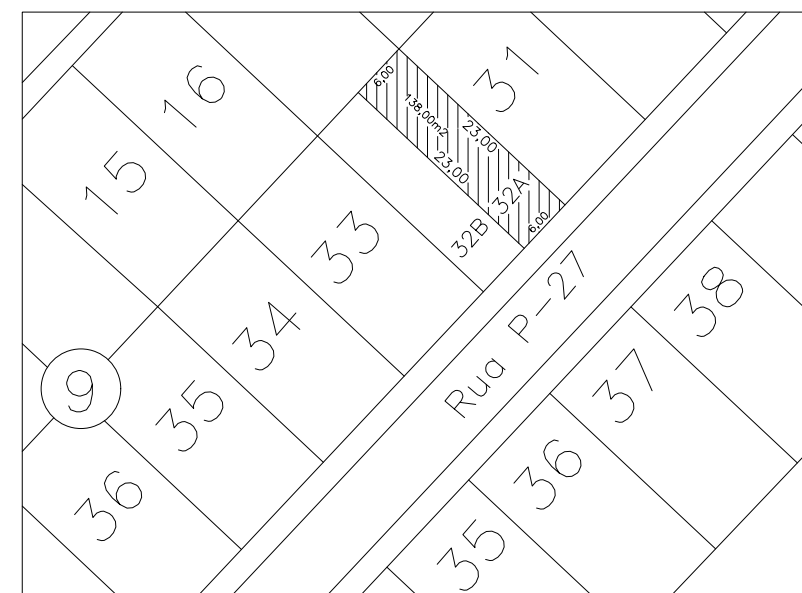


SITUAÇÃO – 1:75

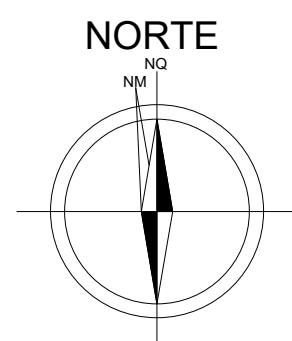

Materiais – Revestimento	
Parede interna	Revestimento grafiato
Parede externa	Textura
Piso interno	Revestimento 60x60
Piso externo	Piso concreto desempenado

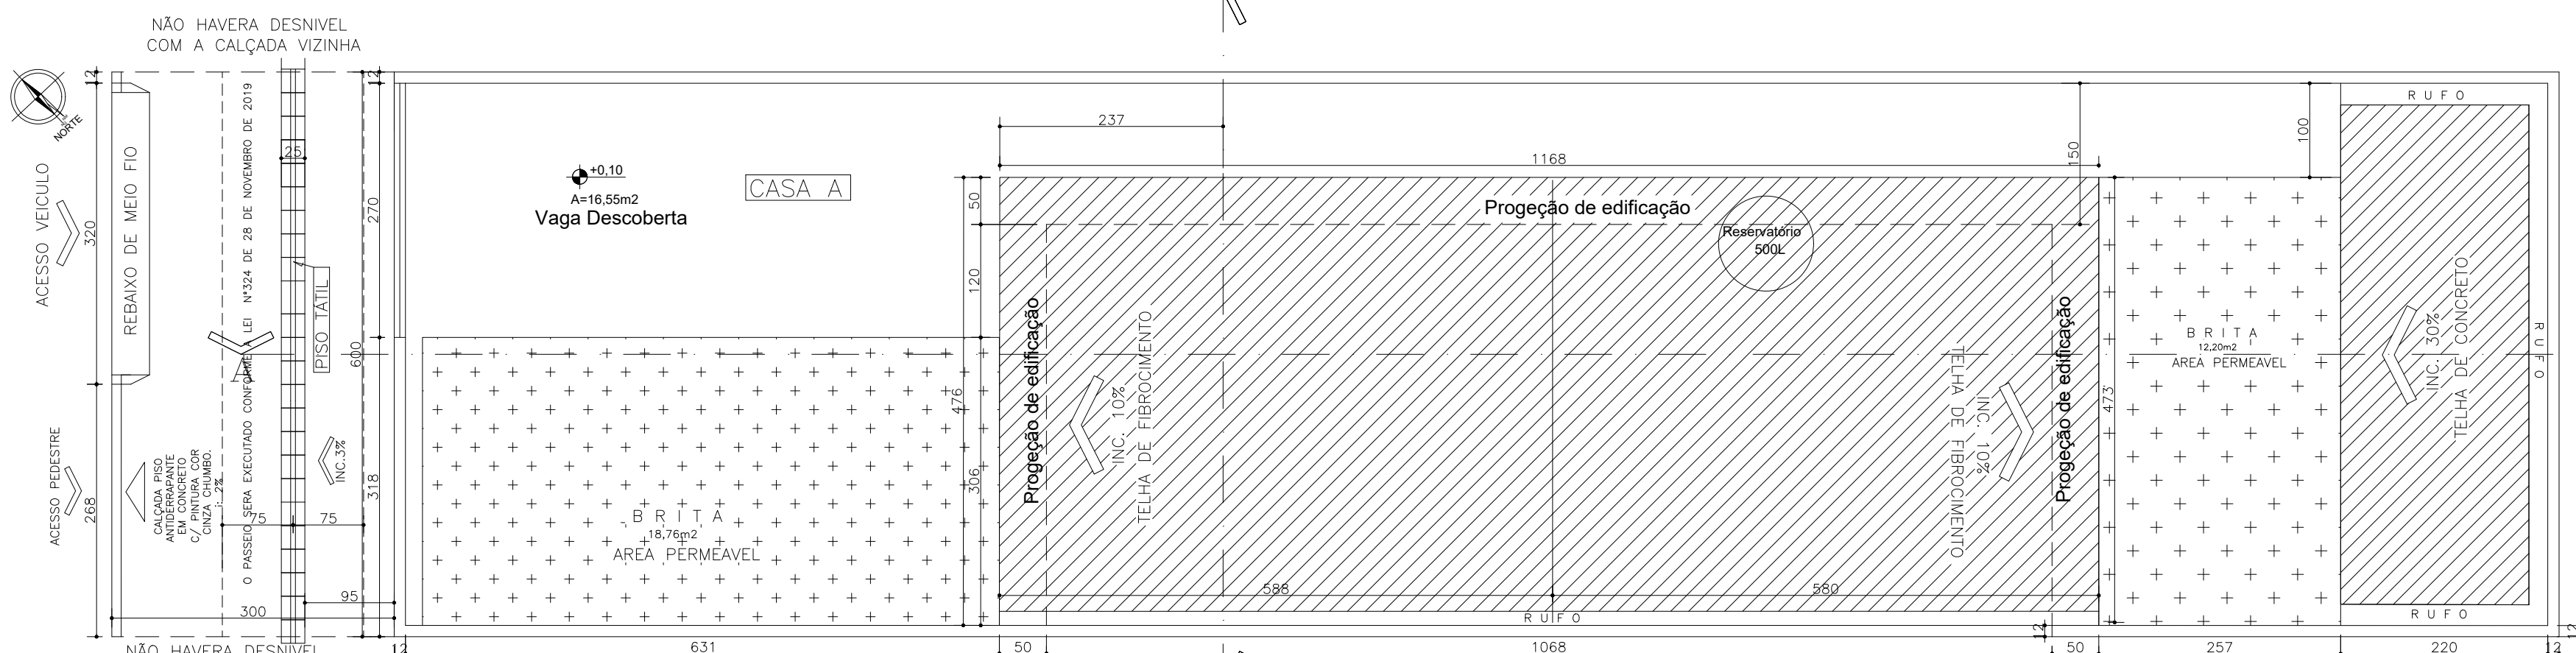

PLANTA DE COBERTURA – 1:100

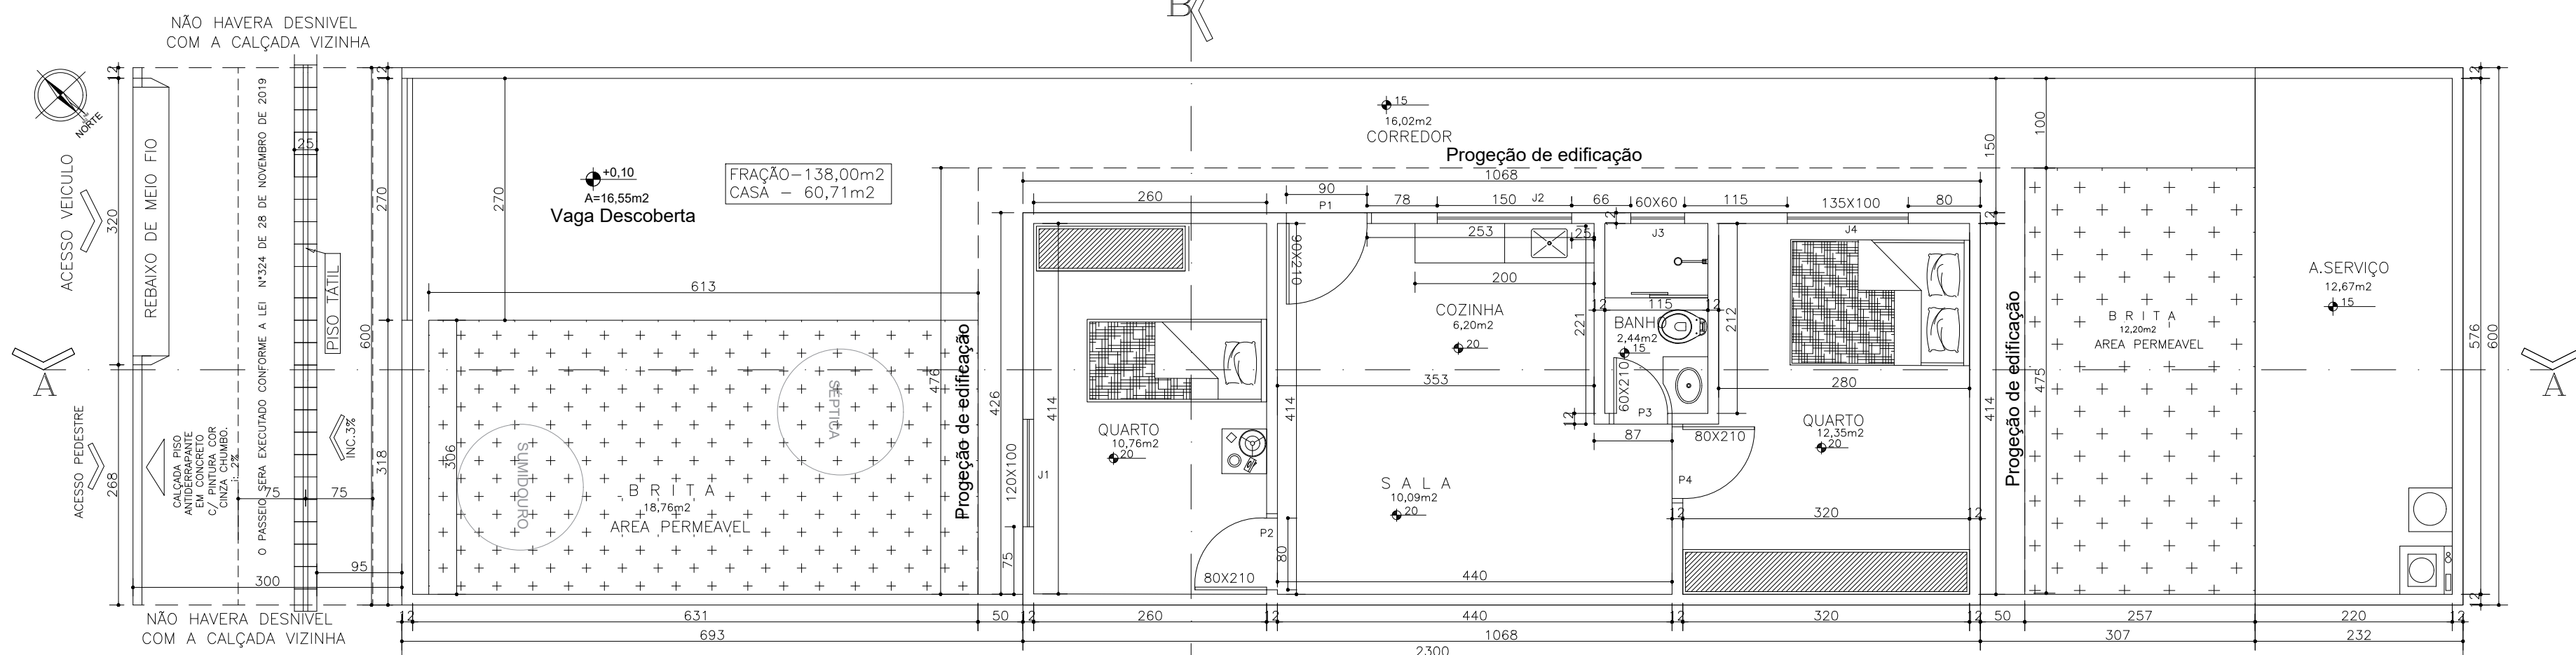

PLANTA BAIXA – 1:75

OBS.:
É DE RESPONSABILIDADE DO PROFISSIONAL ART/RRT
DE EXECUÇÃO E PROJETO, O DETALHE DA CAIXA
INFILTRAÇÃO (RECARGA) E O MEMORIAL DE CALCULO.

PROJETO EXECUTIVO - ARQUITETURA

RUA P-27 Qd.09 Lt.32A - RESIDENCIAL JARDIM PRIMAVERA - ABADIA DE GOIÁS-GO.

Endereço:

RESIDENCIAL 1 UNIDADE
1 PAVTO

Proprietário

IS ENGENHARIA E CONSTRUÇÃO LTDA
CNPJ - 38.111.564/0001-74

Autor do projeto

IAGO FELIPE TOMAZ SERBETO
ENGENHEIRO CIVIL - CREA - Nº 1017361932D-GO

Responsável Técnico

IAGO FELIPE TOMAZ SERBETO
ENGENHEIRO CIVIL - CREA - Nº 1017361932D-GO

LOGOMARCA:



DESCRIÇÃO DOS PAVTOS:

TÉRREO

CONTEUDO:
- PLANTAS ESQUEMÁTICAS
- DE LOCAÇÃO
- CORTES ESQUEMÁTICOS
- PLANTA DE SITUAÇÃO
- CÁLCULO CAIXA DE RECARGA
- QUADRO DE ÁREAS.

ÁREA DO TERRENO ORIGINAL:

138,00M2

ÁREA TOTAL DA CONSTRUÇÃO:

60,71M²

ÁREA PERMEÁVEL

I.P.

30,96m²

0000

I.C.C.A.P.

1,02m³

COBERTURA VEGETAL

COBERTURA VEGETAL

NÃO PERMEÁVEL

01 caixas de recarga

FOLHA:

1/1

DATA:

MAIO/2025