



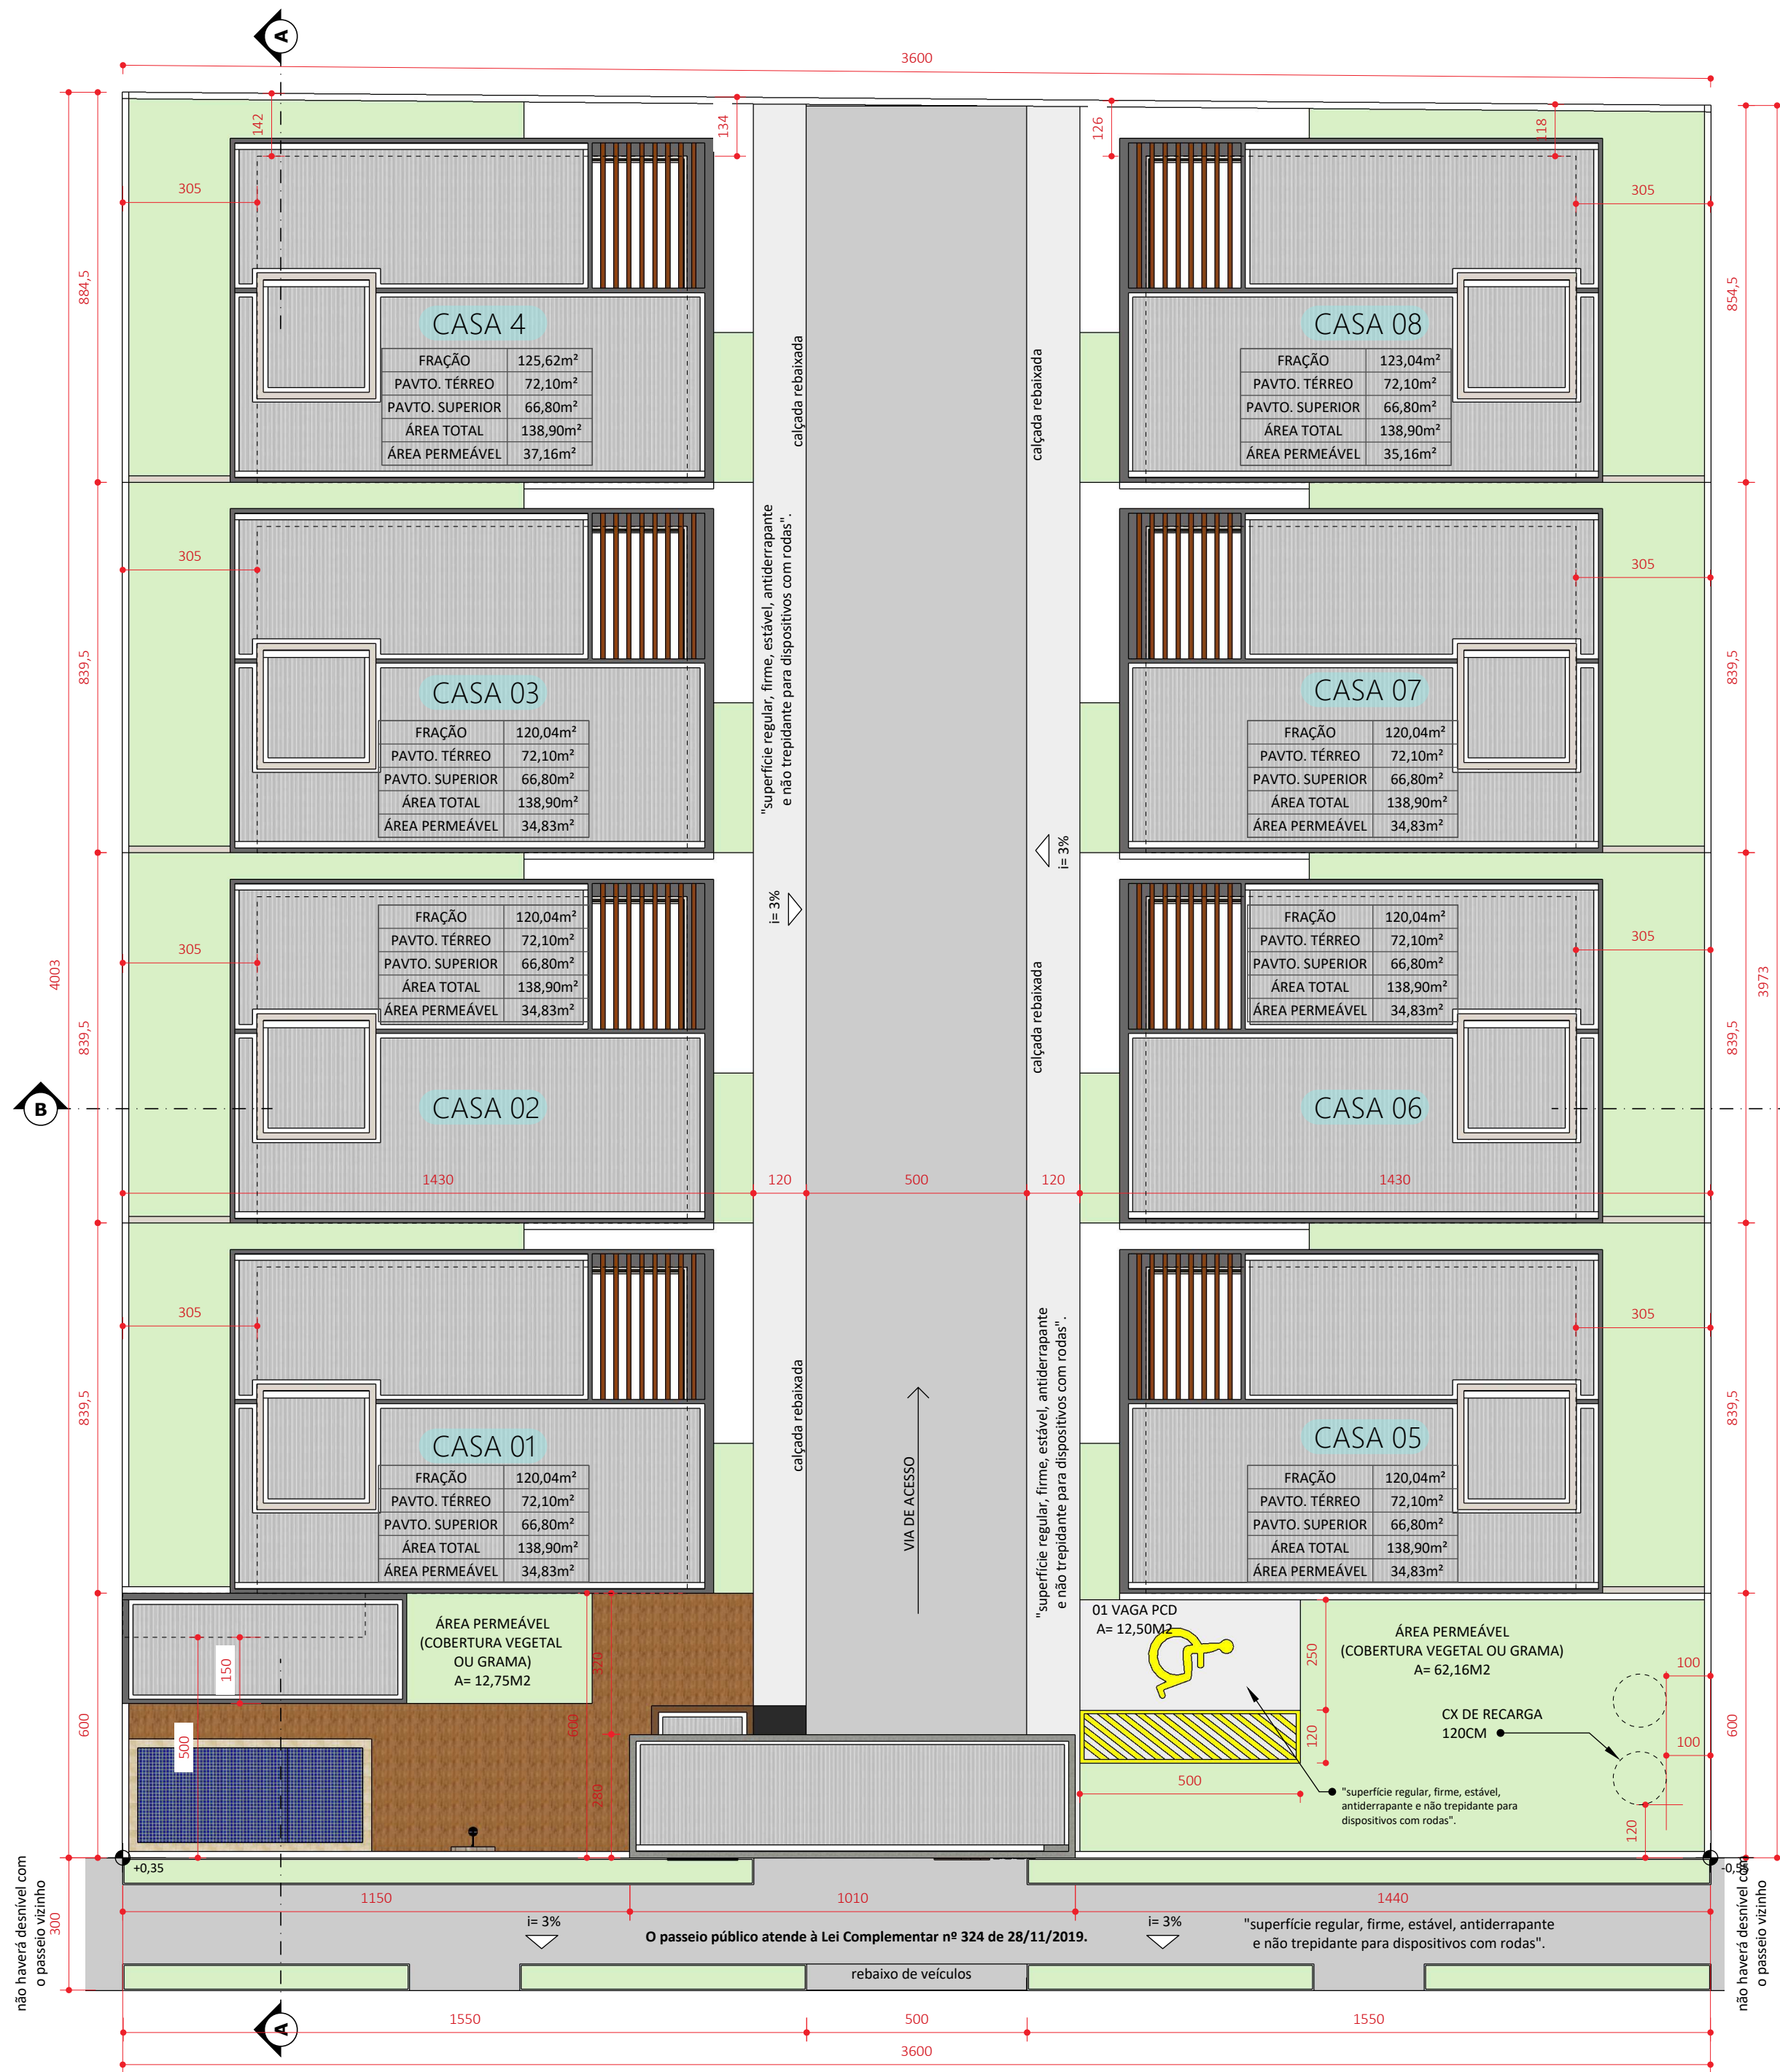


Planta de Locação

Esc.: 1/125

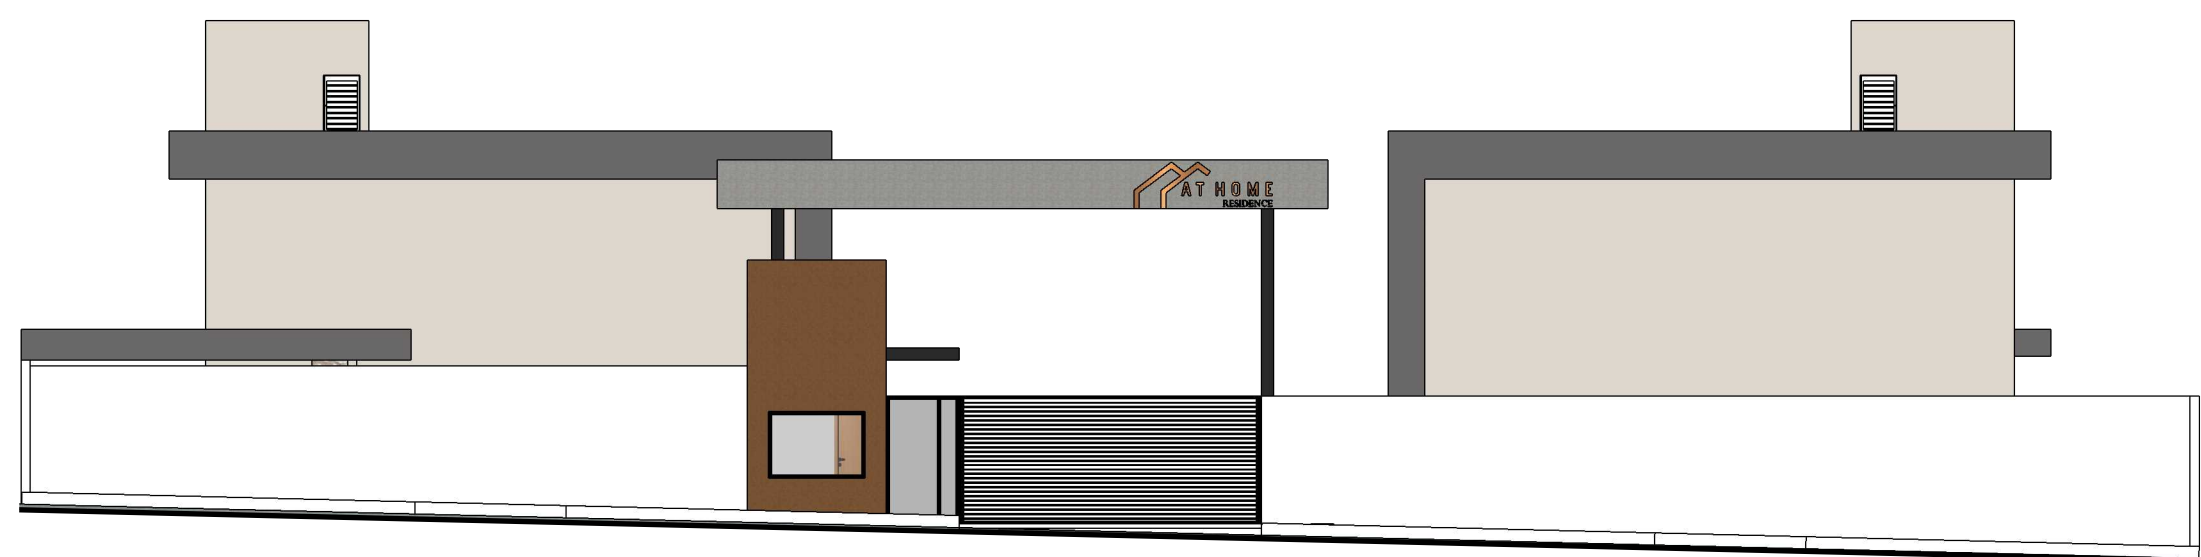


Fachada Frontal

Esc.: 1/125

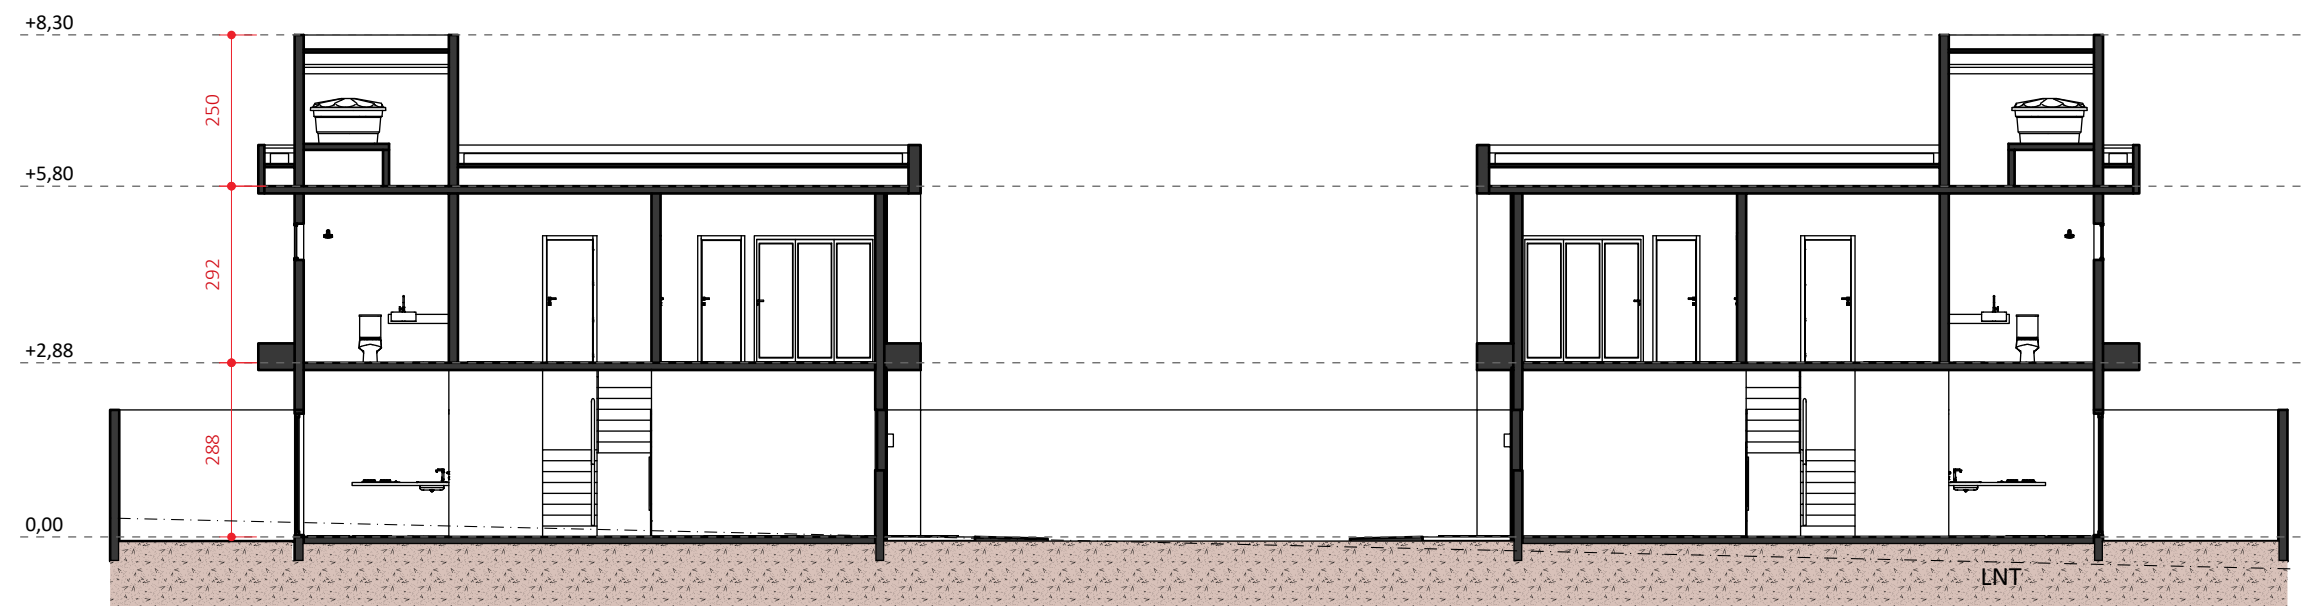

Corte BB- Locação

Esc.: 1/125

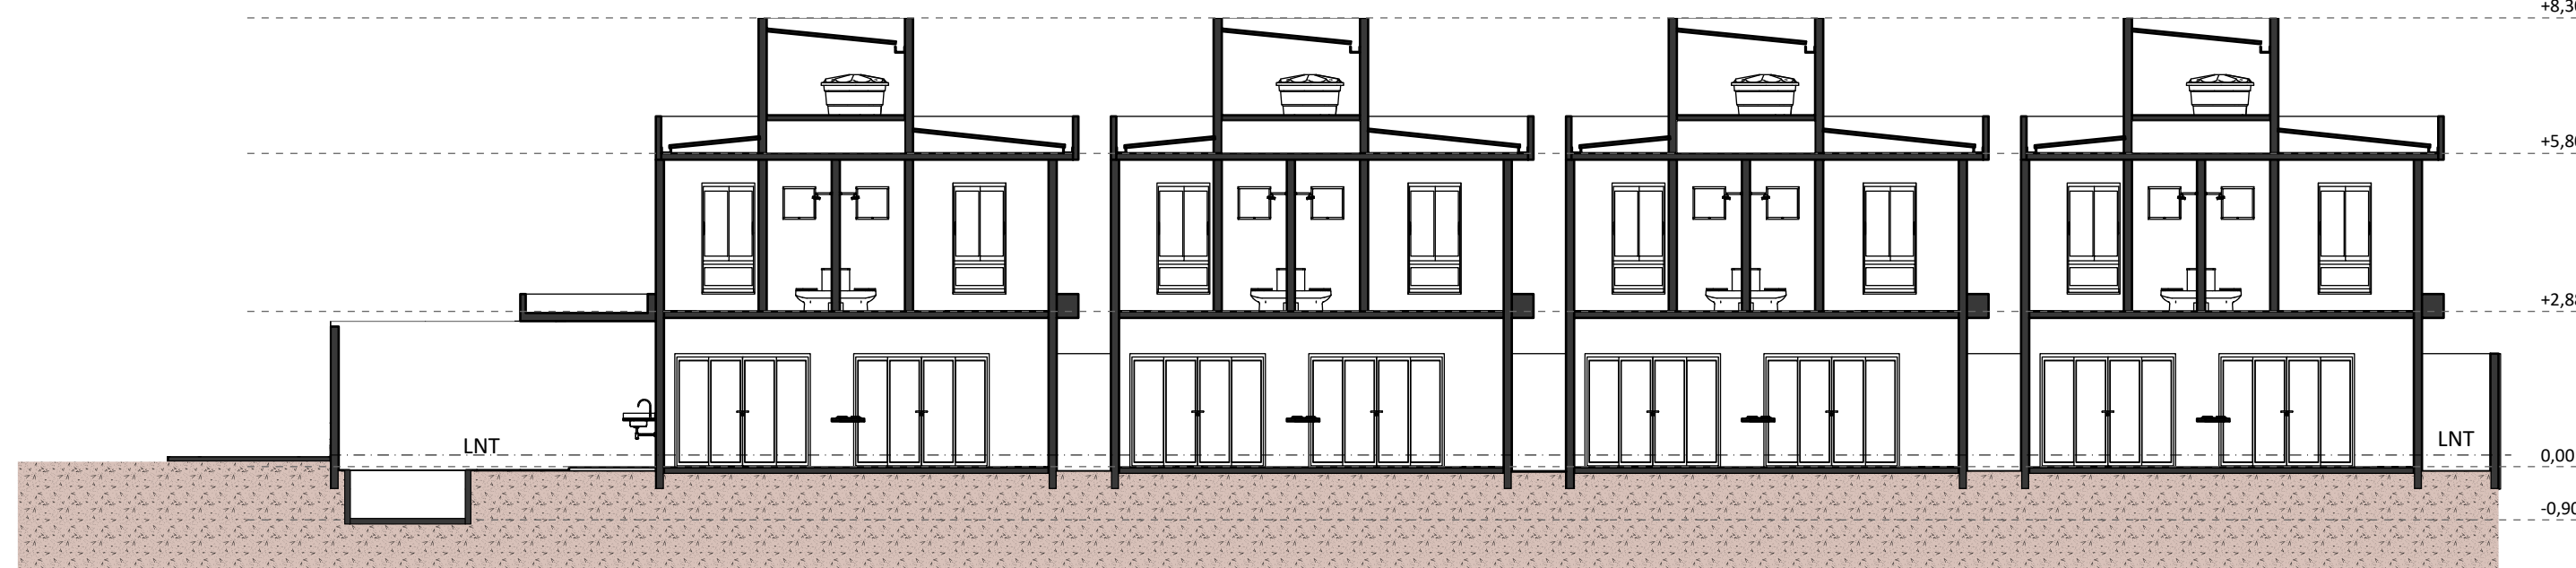

Corte AA- Locação

Esc.: 1/125


Quadro de Áreas

ÁREAS PRIVATIVAS	CASA 01	CASA 02	CASA 03	CASA 04	CASA 05	CASA 06	CASA 07	CASA 08	TOTAL PRIVATIVA	GUARITA	LAZER	TOTAL
FRAÇÃO	120,04m²	120,04m²	120,04m²	125,62m²	120,04m²	120,04m²	120,04m²	123,04m²	968,90m²			
PAVTO. TERREO	72,10m²	72,10m²	72,10m²	72,10m²	72,10m²	72,10m²	72,10m²	72,10m²	576,80m²	28,03m²	9,62m²	614,45m² (42,79%)
PAVTO. SUPERIOR	66,80m²	66,80m²	66,80m²	66,80m²	66,80m²	66,80m²	66,80m²	66,80m²	534,40m²			534,40m²
ÁREA TOTAL	138,90m²	138,90m²	138,90m²	138,90m²	138,90m²	138,90m²	138,90m²	138,90m²	1111,20m²			1148,85m²
ÁREA PERMEÁVEL	34,83m²	34,83m²	34,83m²	37,16m²	34,83m²	34,83m²	34,83m²	35,16m²	281,30m²		74,91m²	356,21m² (24,80%)



Planta de Situação

sem escala

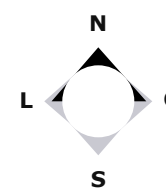

É de responsabilidade do profissional, que assinou a ART/RTT de execução e projeto, o detalhe da Caixa de Infiltração (Recarga) e o Memorial de Cálculo.

I.P.	356,21 24,80%	m²	EM COBERTURA VEGETAL
C.C.A.P.	5,47	m³	02 N° CAIXAS

IP = ÍNDICE PAISAGÍSTICO
C.C.A.P. = ÍNDICE CONTROLE DE CAPTAÇÃO DE ÁGUA PLUVIAL



obs.: a fonte de alimentação das caixas é a cobertura

OBSERVAÇÃO:
1 - TAMPA DE FERRO FUNDIDO
2 - AFASTAMENTO MÍNIMO DAS DIVISAS = 1,00m
DIÂMETRO EM (mm)
DIMENSÕES EM (m)

CÁLCULO
LEI COMPLEMENTAR N.º 246
DE 29 DE ABRIL DE 2013
É NECESSÁRIO 1m³ DE CAIXA DE RECARGA
PARA CADA 200,00 m²
PROFUNDIDADE MÁX. 2,60m

ÁREA DE INFILTRAÇÃO NECESSÁRIA
200,00 m² - 1 m³
1079,59m² - 5,39m³

VOLUME PARA INFILTRAÇÃO
VOLUME TOTAL = C . L . A
C = COMPRIMENTO
L = LARGURA
A = ALTURA
VOLUME TOTAL = 1,20 x 1,20 x 1,90 = 2,736 m³

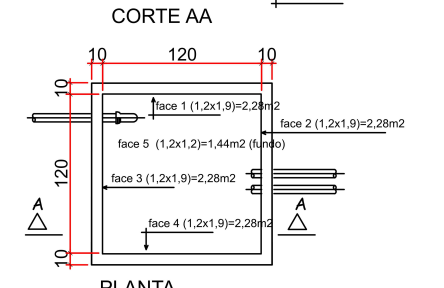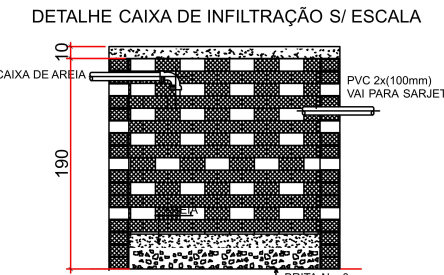

PLANTA

- "O PROJETO ATENDE ÀS REGRAS PREVISTAS NAS NORMAS TÉCNICAS DE ACESSIBILIDADE: ABNT NBR 9050/2020, LEI Nº 10.098/2000, DECRETO Nº 5.296 DE DEZ/2004, LEI Nº 13.146/2015, LEI Nº 324 DE NOV/2019, E DEMAIS PERTINENTES";
- "O MEMORIAL DE CÁLCULO DA CAIXA DE INFILTRAÇÃO (RECARGA) É DE RESPONSABILIDADE DO PROFISSIONAL QUE ASSINOU A ART/RTT DE EXECUÇÃO E PROJETO";
- DE ACORDO COM A LEI COMPLEMENTAR 302 DE DEZ/2016, "É DE RESPONSABILIDADE DO PROPRIETÁRIO OU INTERESSADO A APROVAÇÃO DO PROJETO JUNTO AO CORPO DE BOMBEIROS MILITAR DO ESTADO DE GOIÁS, E NO ATO DA EMISSÃO DA CERTIDÃO DE CONCLUSÃO DE OBRA, DEVERÁ SER APRESENTADO O CERTIFICADO DE CONFORMIDADE OU SIMILAR EMITIDO PELO MENSIONADO ÓRGÃO".

APROVAÇÃO:

PROCESSO N.º PROJETO N.º 26830

PREFEITURA DE GOIÂNIA
SECRETARIA MUNICIPAL DE PLANEJAMENTO
URBANO E HABITAÇÃO-SEPLANH
DIRETORIA DE ANÁLISE E
APROVAÇÃO DE PROJETOS

APROVADO

EM/...../.....

PROJETO LEGAL ARQUITETURA APROVAÇÃO

Endereço: -RUA MACHADO DE ASSIS, QUADRA 10 LOTE 25-27-29, BAIRRO ANHANGUERA, GOIÂNIA-GO

HABITAÇÃO SERIADA- 08UN
02 PAVTOS

Proprietário IS ENGENHARIA EIRELI CNPJ: 38.111.564/0001-74

Autor do projeto CAPA ARQUITETURA E SERVICOS Ltda. CNPJ 43.179.866/0001-14

Responsável Técnico IS ENGENHARIA EIRELI CNPJ: 38.111.564/0001-74

LOGOMARCA:



(62) 9 9820 0225 / (62) 9 8257 5577
contato@capaang.com.br
Avenida E, nº1470, sala 1011, Ed. JK
New Concept Business, 3d, Goiás,
Goiânia, GO, CEP: 74810-030

DESCRIÇÃO DOS PAVTOS:

TÉRREO + SUPERIOR

CONTEÚDO:
PLANTA DE LOCAÇÃO
FACHADA FRONTAL
CORTE AA
CORTE BB
QUADRO DE ÁREAS
PLANTA DE SITUAÇÃO

ÁREA DO TERRENO ORIGINAL:
1435,80 m²
ÁREA TOTAL DA CONSTRUÇÃO:
1.148,85M²
ÍNDICE CONTROLE CAPTAÇÃO
ÁGUA PLUVIAL:
5,47m² (02 caixas)
ÍNDICE PAISAGÍSTICO:
356,21m² (24,80%)
ARQUIVO:
COND-PROJ.LEGAL-DET.R00

FOLHA:
1/5
DATA:
DEZ 2022
DESENHO:
REVISÃO 02