
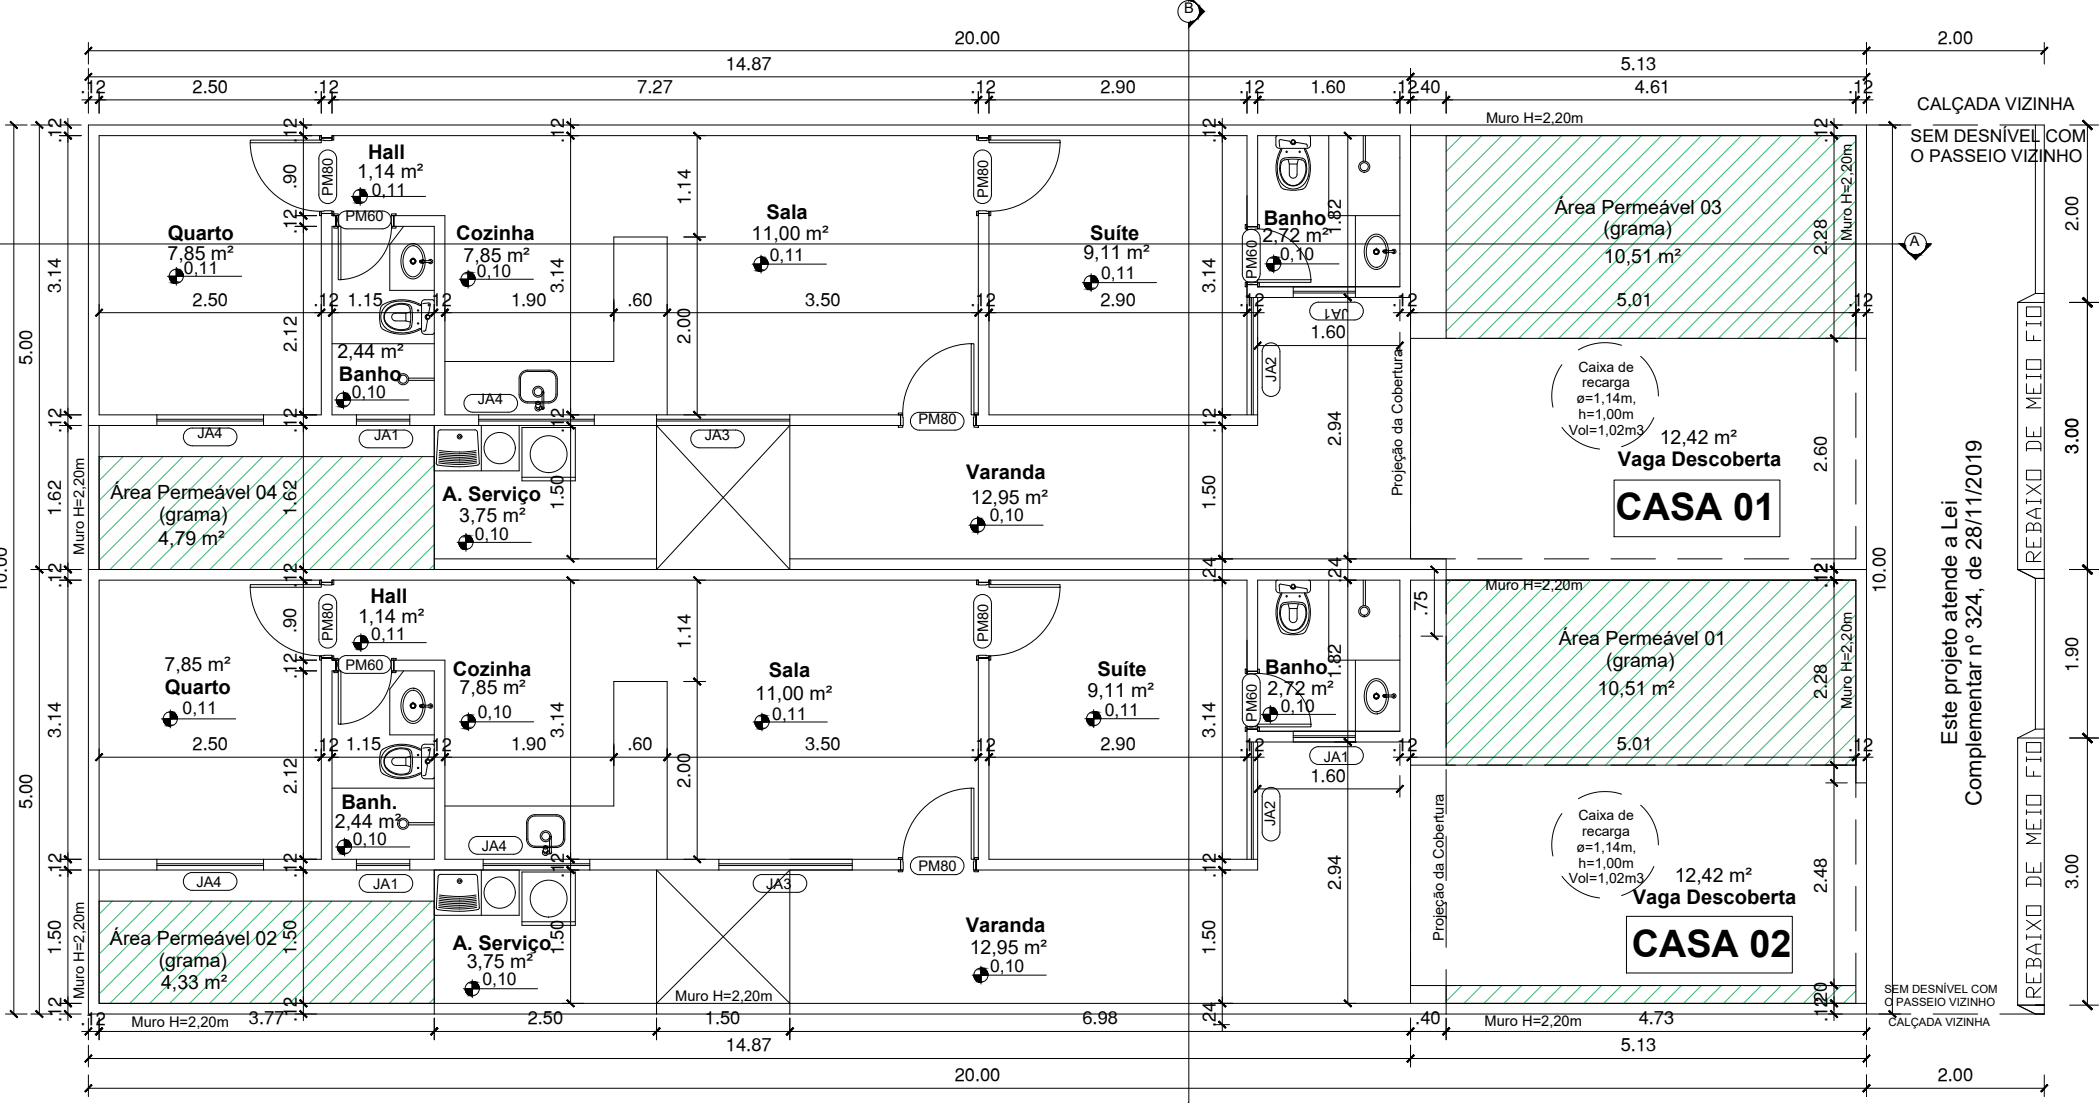
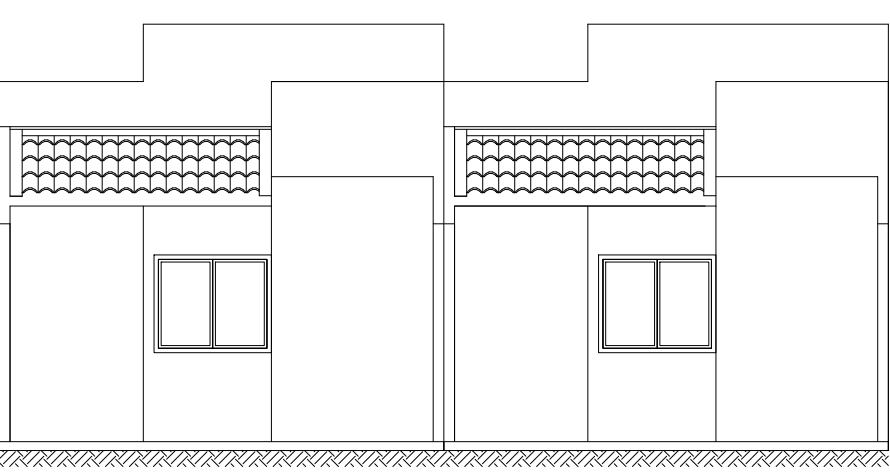
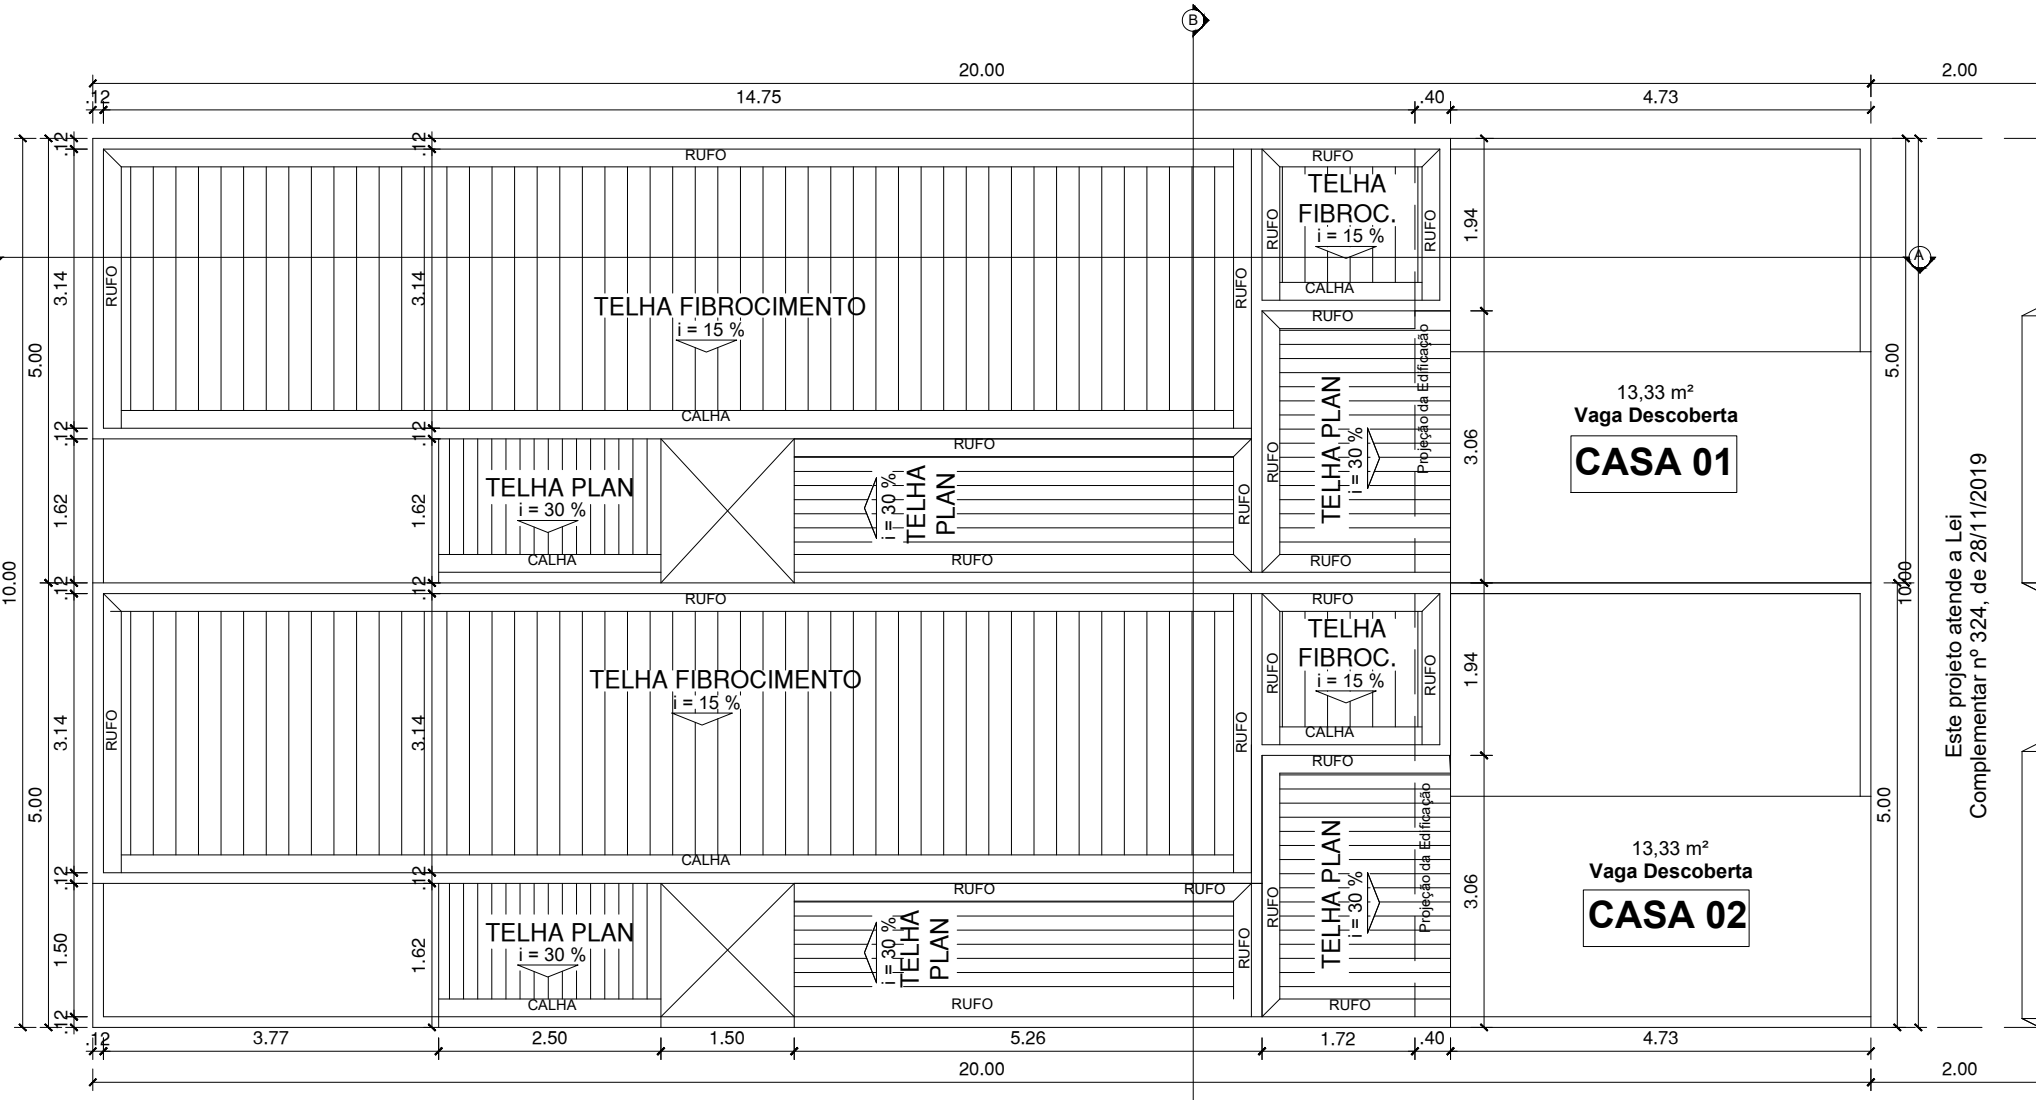
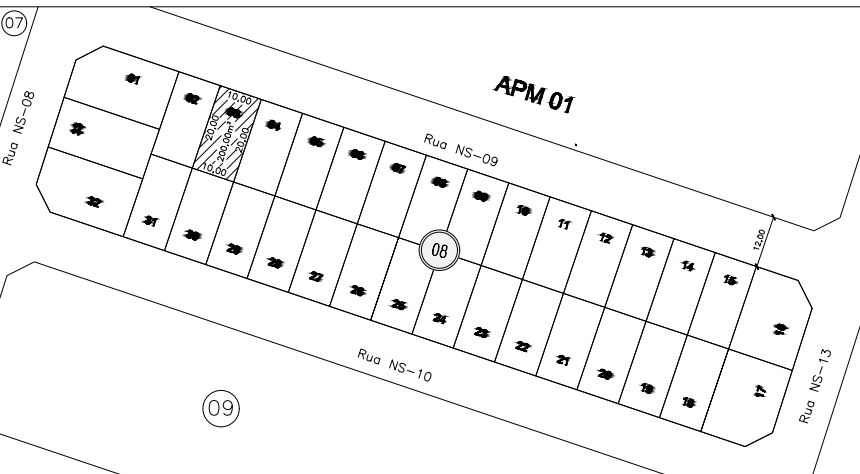
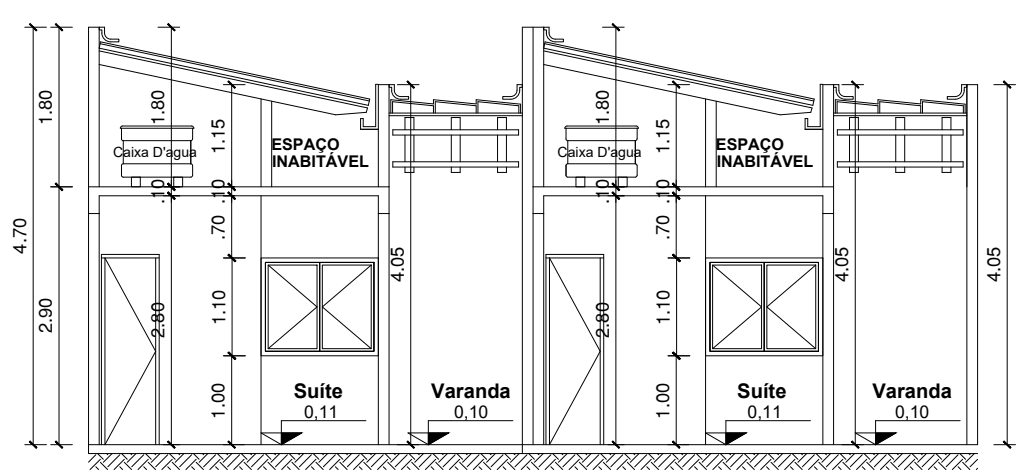


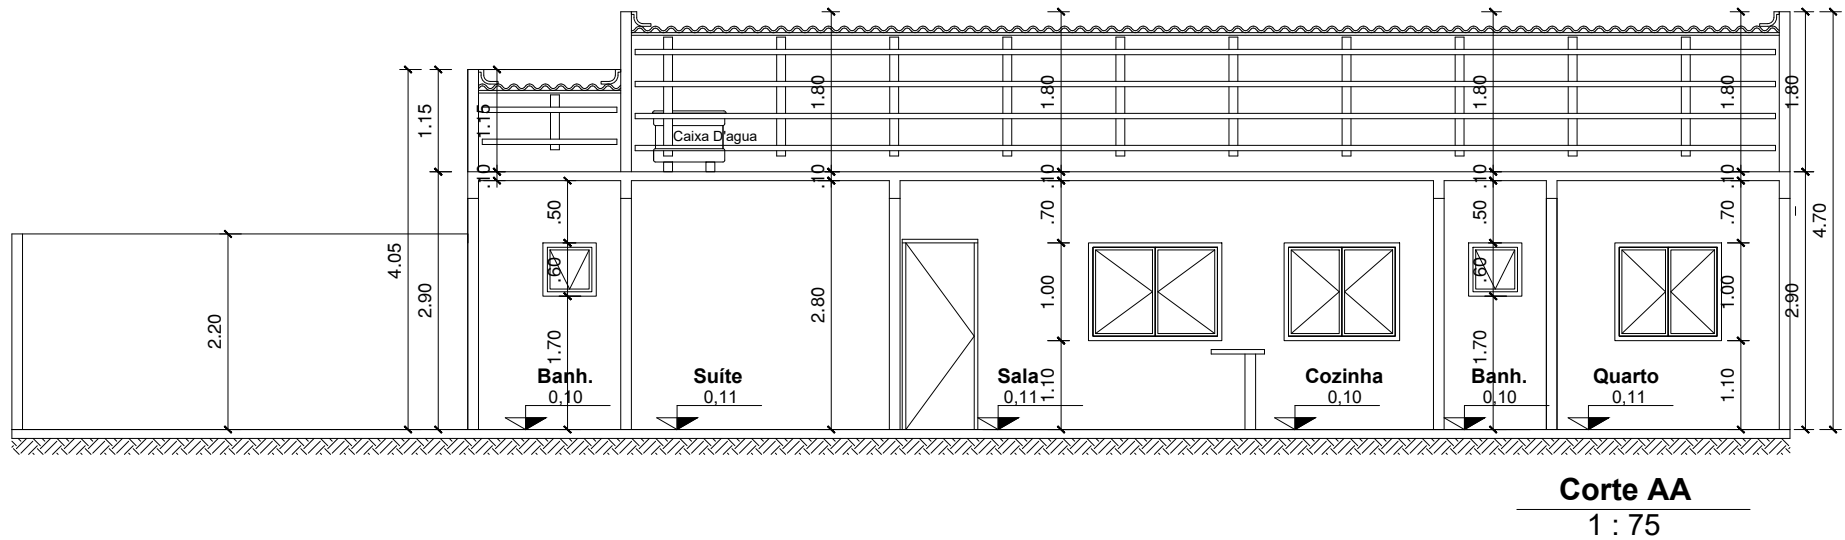

QUADRO DE ABERTURAS - JANELAS				
LEG	LARGURA	ALTURA	PEITRIL	ÁREA
JA1	0.60	0.60	1.70	0.36
JA2	1.20	1.00	1.10	1.2
JA3	1.20	1.00	1.10	1.2
JA4	1.20	1.00	1.10	1.2

QUADRO DE ÁREAS – HABITAÇÃO UNIFAMILIAR					
UNIDADE	PAV. TERREJO	TOTAL	ÍNDICE PAISAGÍSTICO	TERRENO	VAGA
CASA 1	65,62m²	65,62m²	14,84m² Em cob. vegetal	100,00m²	01
CASA 2	65,62m²	65,62m²	15,30m² Em cob. vegetal	100,00m²	01
T O T A L	131,24m²	131,24m²	30,14m² Em cob. vegetal	200,00m²	02

A. IMPERMEABIL. 169,68m².200>0,85m². EM 2 CAIXAS DE RECARGA= 01,14 / H - 1,00m=1,02m³

QUADRO DE ÁREAS	
ÁREA DO TERRENO	200.00m²
ÁREA CONSTRUIDA	131.24m²
ÁREA PERMEÁVEL	30.14m²
NÚMERO DE VAGAS DE ESTACIONAMENTO	02

MEMORIAL DE CÁLCULO DA CAIXA DE RECARGA			
(ÍNDICE DE CONTROLE DE CAPTAÇÃO DE ÁGUAS PLUVIAIS NA PROPORÇÃO DE 1 m² DE CAIXA DE RECARGA PARA CADA 200m² DE TERRENO IMPERMEABILIZADO - ART. 128 L.C. 171/2008)			
ÁREA DO TERRENO	200.00m²		
ÍNDICE PAISAGÍSTICO (COBERTURA VEGETAL PERMEÁVEL)	30.14m²		
ÍNDICE PAISAGÍSTICO (COBERTURA VEGETAL NÃO PERMEÁVEL)	0.0000m²		
ÁREA IMPERMEABILIZADA	169.86m²		
VOLUME NECESSÁRIO DA CAIXA DE RECARGA	0.86m³		
DIMENSÕES DA CAIXA DE RECARGA			
ÁREA DA BASE	1.02m²	Nº DE CAIXAS	2 UNIDADES
ALTURA	1.00m	VOLUME TOTAL	2.04m³
VOLUME UNITÁRIO	1.02m³		

- NOTAS:
- O PROJETO ATENDE AO PLANO DIRETOR E AO CÓDIGO DE OBRAS E EDIFICAÇÕES DE GOIÂNIA - LEI COMPLEMENTAR 349/2022 E LEI COMPLEMENTAR 364/2023, E SEUS REGULAMENTOS;
 - O PROJETO ATENDE AS REGRAS PREVISTAS NAS NORMAS TÉCNICAS DE ACESSIBILIDADE: ABNT 9050/2020, LEI Nº 10.098/2000, DECRETO FEDERAL Nº 5.296/2004, LEI Nº 13.146/2015 E LEI COMPLEMENTAR Nº 324/2019;
 - É DE RESPONSABILIDADE DO PROFISSIONAL QUE ASSINOU A ART/RT DE EXECUÇÃO E PROJETO O DETALHAMENTO DA CAIXA DE INFILTRAÇÃO (RECARGA DO LENÇOL FREÁTICO) E O MEMORIAL DE CÁLCULO;
 - NÃO EXISTEM ABERTURAS SOBRE AS DIVISAS LATERAIS E DE FUNDO DO TERRENO, NEM BEM COMO A MENOS DE 1,50m DOS MESMOS, E A MENOS DE 0,75m PERPENDICULARMENTE A ESTES.

APROVAÇÃO RESPONSÁVEL

LEI COMPLEMENTAR Nº 302/2016 - DECRETO Nº 1551/2017 - INSTRUÇÃO NORMATIVA Nº 003/2022 - SEPLANH

ARQUITETURA-PROJETO SIMPLIFICADO

Endereço: RUA NS-09, QD. 08, LT. 03, RES. NOSSA SENHORA AUXILIADORA - GOIÂNIA - GO, IPTU Nº 338.168.0272.000-0, USO DO SOLO Nº UDS0208080213

Proprietário: IS ENGENHARIA E CONSTRUÇÃO LTDA, CNPJ - 38.111.564/0001-74

Autor do projeto: IAGO FELIPE TOMAZ SERBETO, ENGENHEIRO CIVIL - CREA - Nº 1017361932D-GO, CAE Nº 4791223, IS ENGENHARIA E CONSTRUÇÃO LTDA, CNPJ - 38.111.564/0001-74, CAE Nº 5372619

Responsável Técnico: IAGO FELIPE TOMAZ SERBETO, ENGENHEIRO CIVIL - CREA - Nº 1017361932D-GO, CAE Nº 4791223

LOGOMARCA:	DESCRIÇÃO DOS PAVTOS:		FOLHA:
	TERREJO		
CONTEÚDO: - PLANTAS ESQUEMÁTICAS - DE LOCAÇÃO - CORTES ESQUEMÁTICOS - PLANTA DE SITUAÇÃO - CÁLCULO CAIXA DE RECARGA - QUADRO DE ÁREAS.	ÁREA DO TERRENO ORIGINAL: 200.00m²	ÁREA TOTAL DA CONSTRUÇÃO: 131.24m²	1/1 DATA: DEZEMBRO/2025
	ÁREA PERMEÁVEL: 30.14m²	COBERTURA VEGETAL 0.0000m²	
	I.P.: 0.0000m²	COBERTURA VEGETAL 0.0000m²	
	I.C.A.P.: 2.04m³	2 caixas de recarga	